


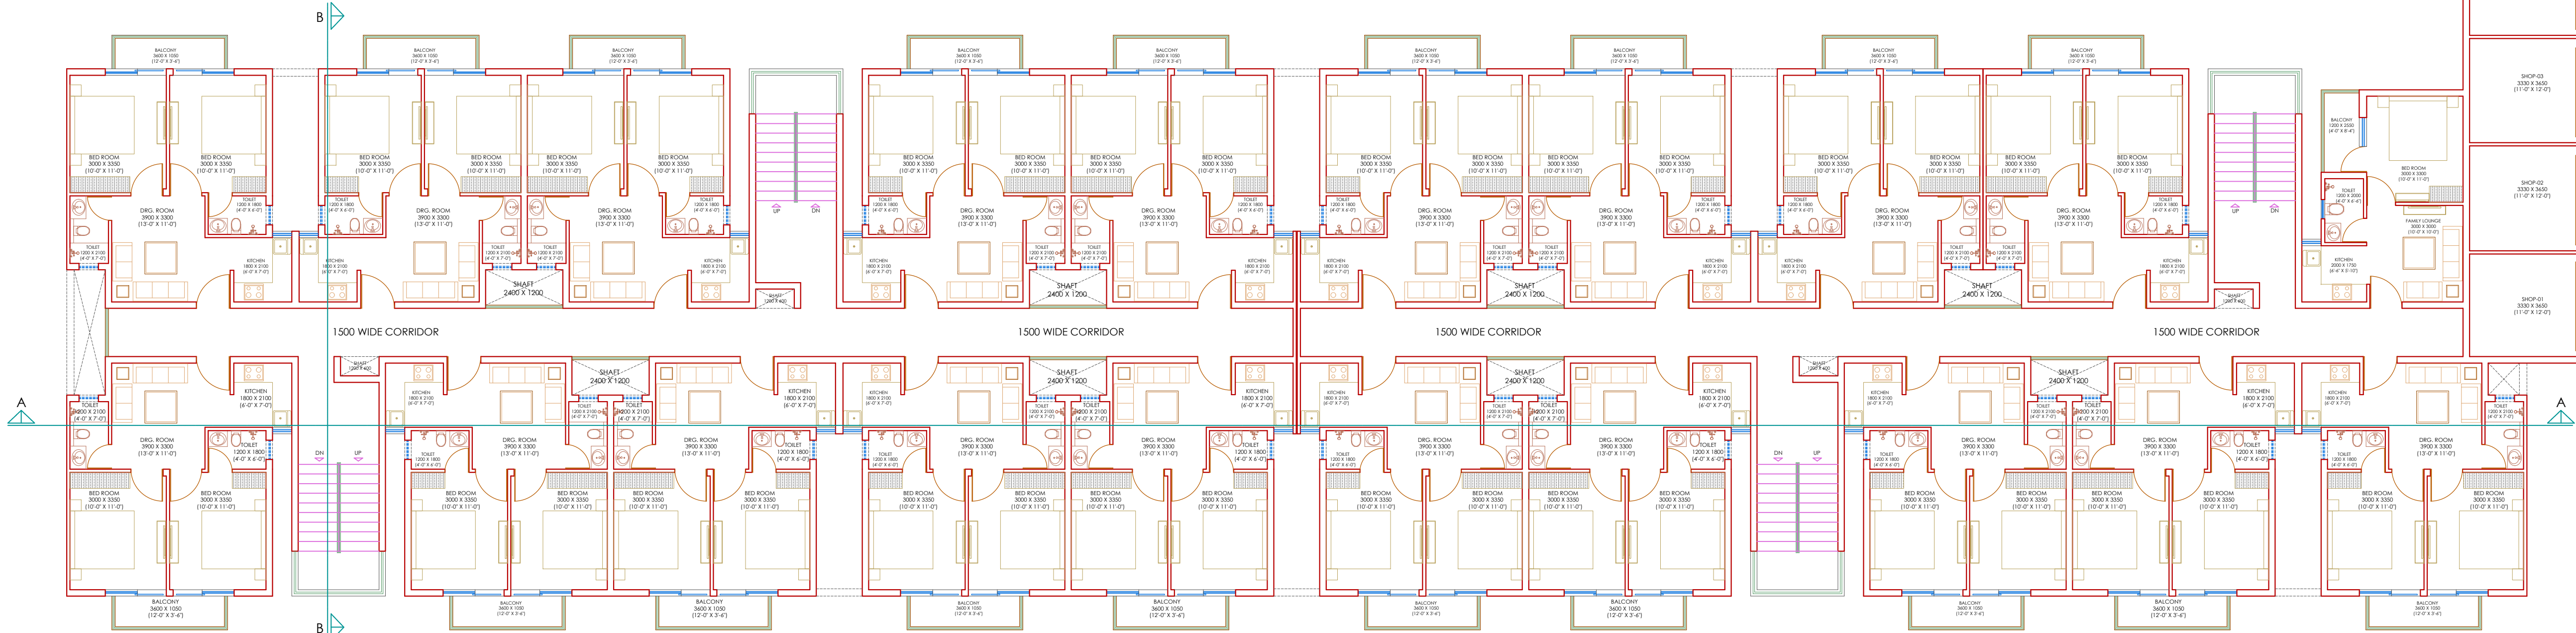


GROUND FLOOR PLAN (TOWER-B1)

GROUND FLOOR PLAN (TOWER-B)




GROUND FLOOR PLAN (TOWER-A1)

GROUND FLOOR PLAN (TOWER-A)

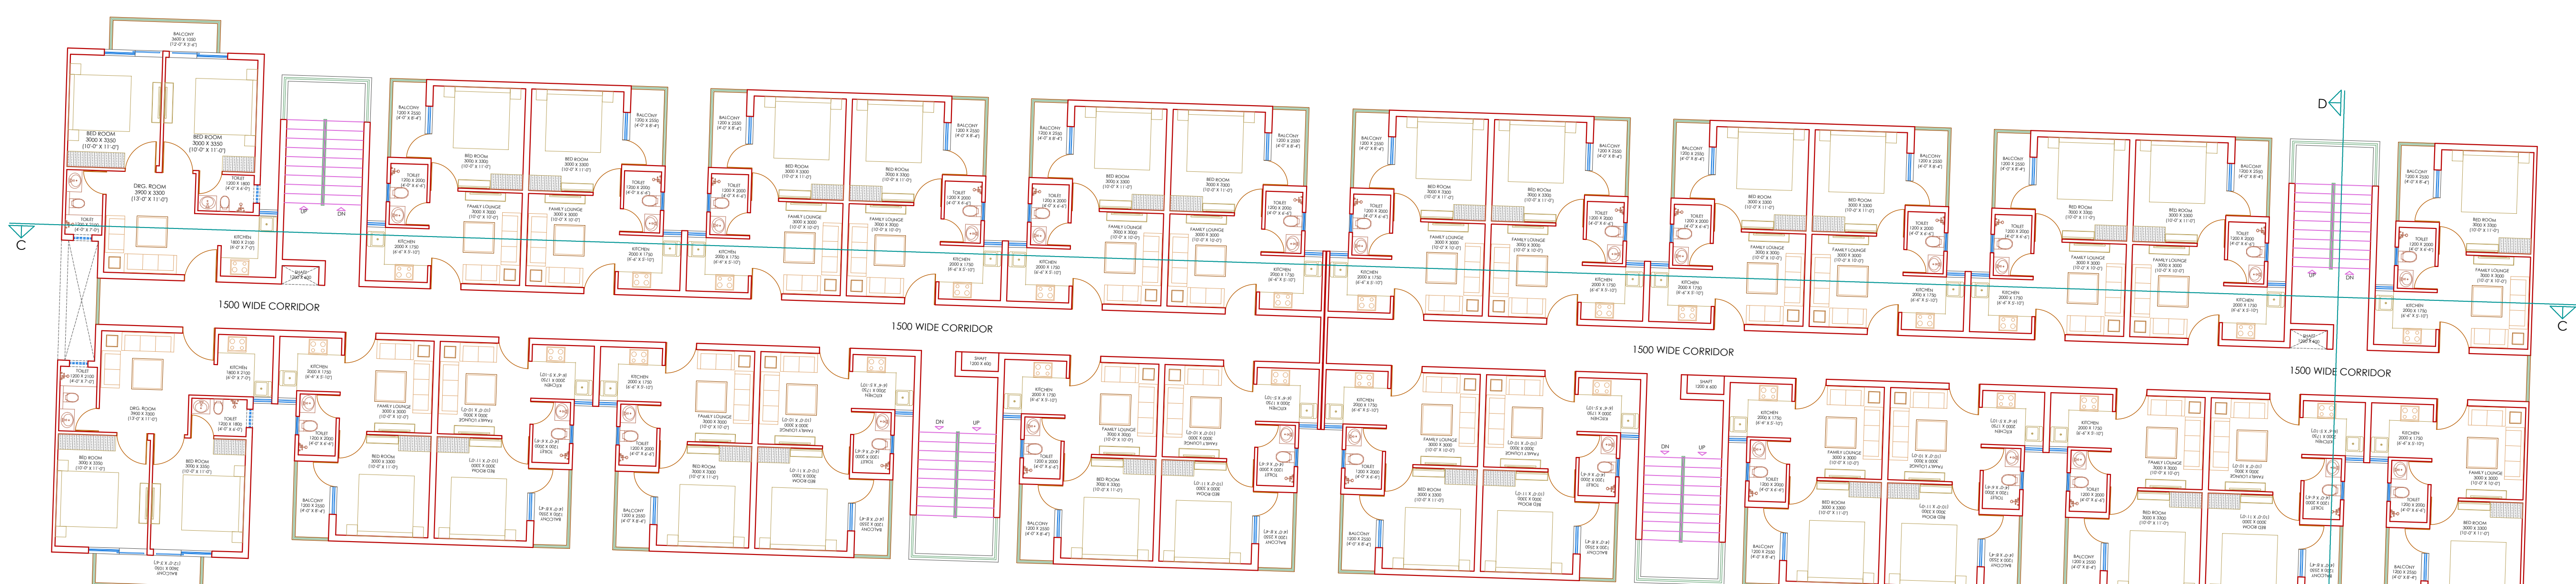

GROUND FLOOR PLAN (TOWER-B1)


GROUND FLOOR PLAN (TOWER-B)

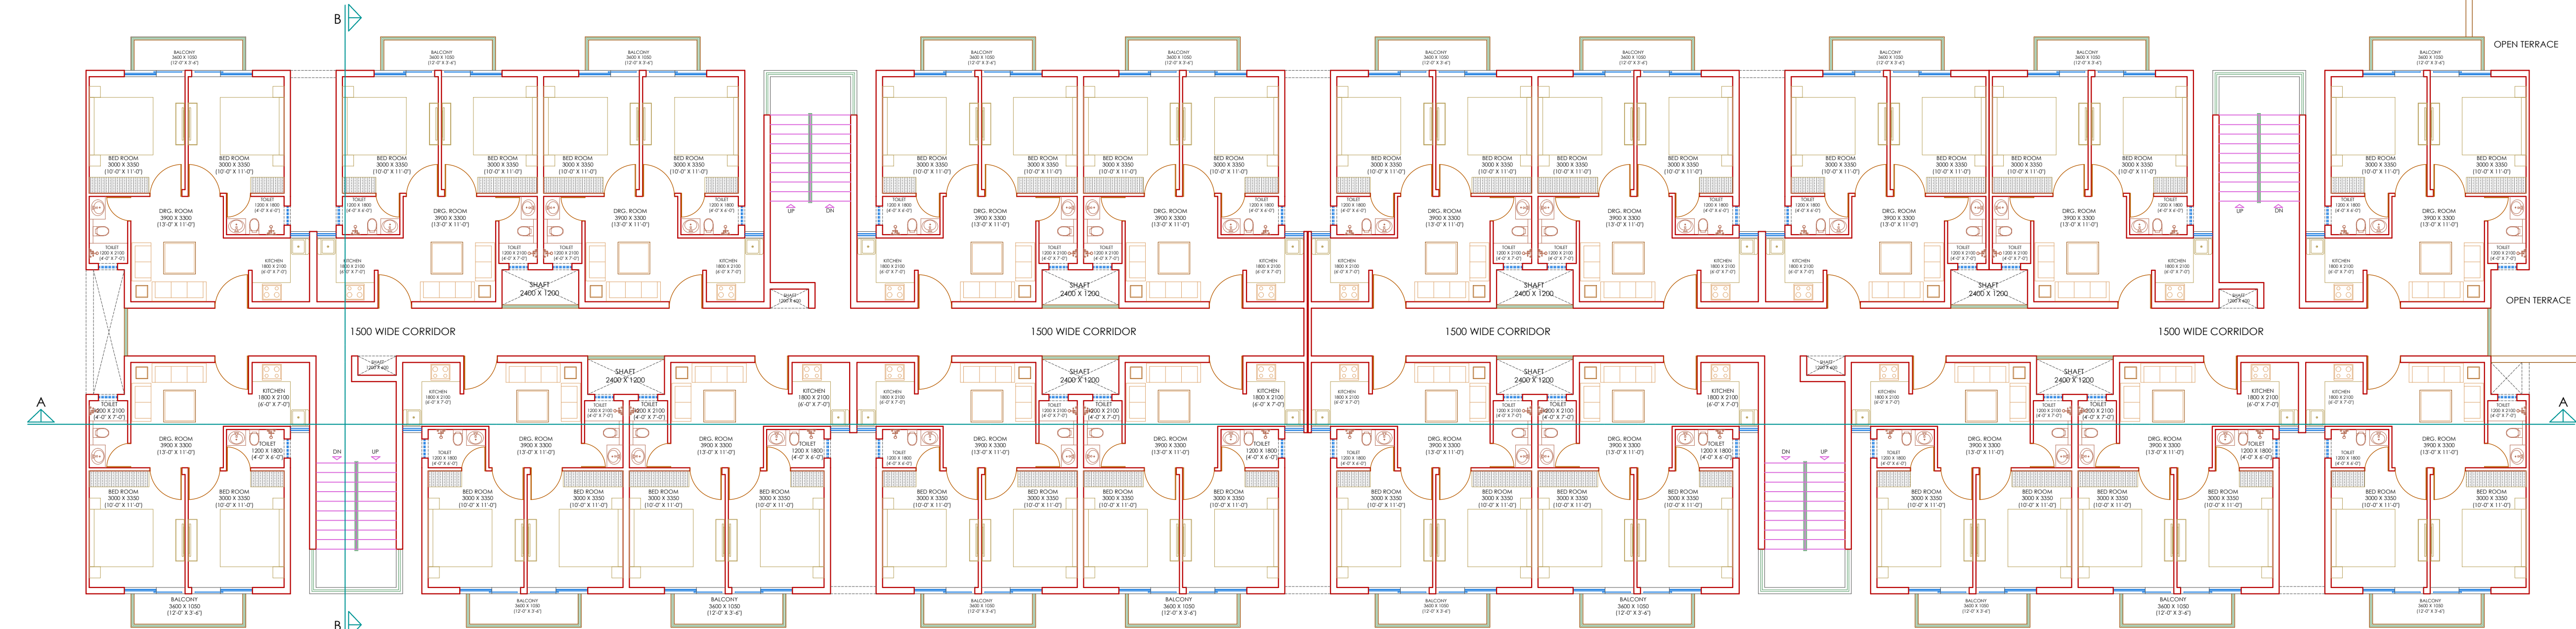

GROUND FLOOR PLAN (TOWER-A1)

GROUND FLOOR PLAN (TOWER-A)

UNIT PLAN

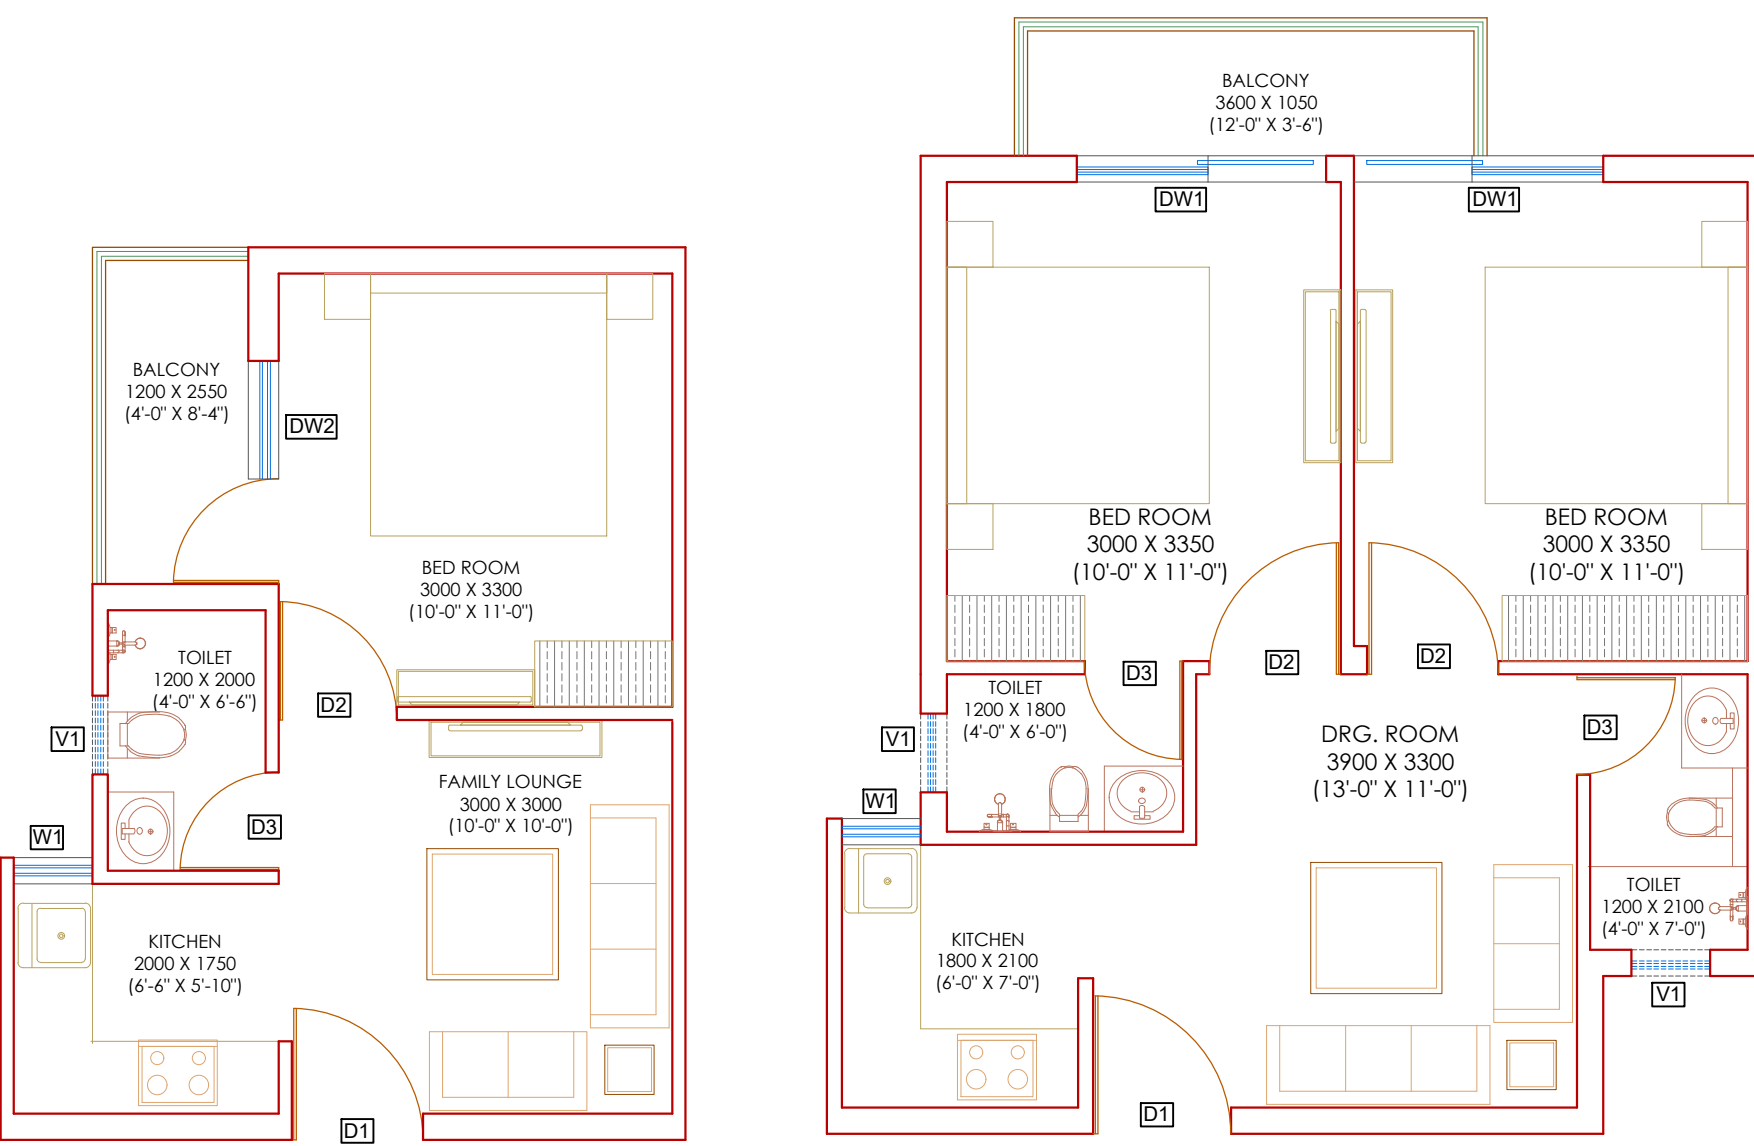


UNIT PLAN (EWS)


(a) BUILT UP AREA = 32.20 SQMT. (WITH BALCONY)
(b) BALCONY = 3.34/2 = 1.67 SQMT. (50%)
(c) BUILT UP AREA = 30.53 SQMT. / 328.62 SQ.FT.
(d) PASSAGE & STAIRCASE = 7.00 SQMT.
(e) SUPER BUILT UP AREA = 37.53 SQMT. / 404.00 SQ.FT.
(f) CARPET AREA = 25.50 SQMT. / 274.50 SQ.FT.

UNIT PLAN (LIG)

(a) BUILT UP AREA = 51.00 SQMT. (WITH BALCONY)
(b) BALCONY = 3.78/2 = 1.89 SQMT. (50%)
(c) BUILT UP AREA = 49.11 SQMT. / 528.60 SQ.FT.
(d) PASSAGE & STAIRCASE = 9.90 SQMT.
(e) SUPER BUILT UP AREA = 59.01 SQMT. / 635.20 SQ.FT.
(f) CARPET AREA = 43.00 SQMT. / 462.85 SQ.FT.

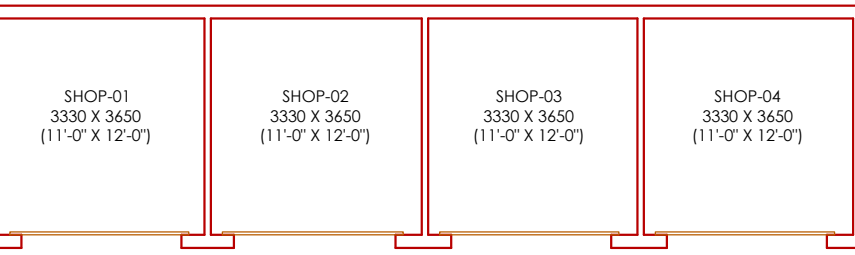

COMMERCIAL LAYOUT

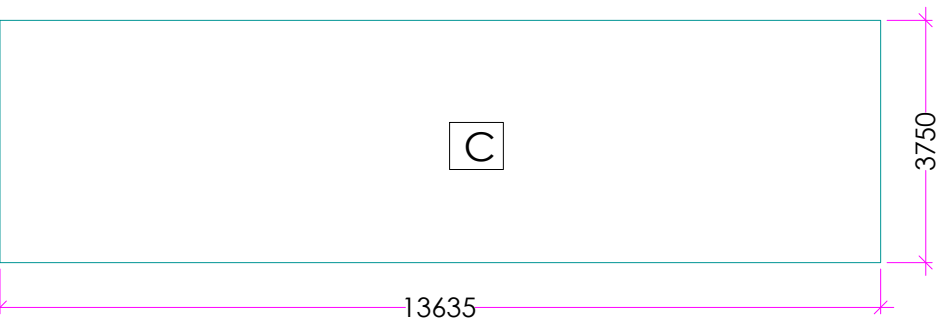

COMMERCIAL AREA DIAGRAM

AREA STATEMENT GROUND FLOOR (COMMERCIAL)						
1.TYPICAL FLOOR						
S.NO.	SHAPE	LENGTH	WIDTH	AREA (SQMT.)	QTY. IN NOS.	AREA (SQMT.)
C	RECTANGLE	13.635	3.750	51.131	1	51.131
TOTAL						51.131

Signature of Owner Signature of Architect

PROJECT

PROPOSE HOUSING UNDER
CM JAN AWAS YOJNA
M/S GENNXT INFRA TECH PVT. LTD.
AT KHASRA NO. 212,213, VILLAGE -
NEEMRANA,TEH. NEEMRANA,DIST.ALWAR (RAJ.)


TOWER - A, A1 & B, B1
FLOOR PLANS AND COMMERCIAL
LAYOUT ,AREA DIAGRAM

SHEET NO


04/04

dmn. : date :
22.11.2022


dlt. : scale :

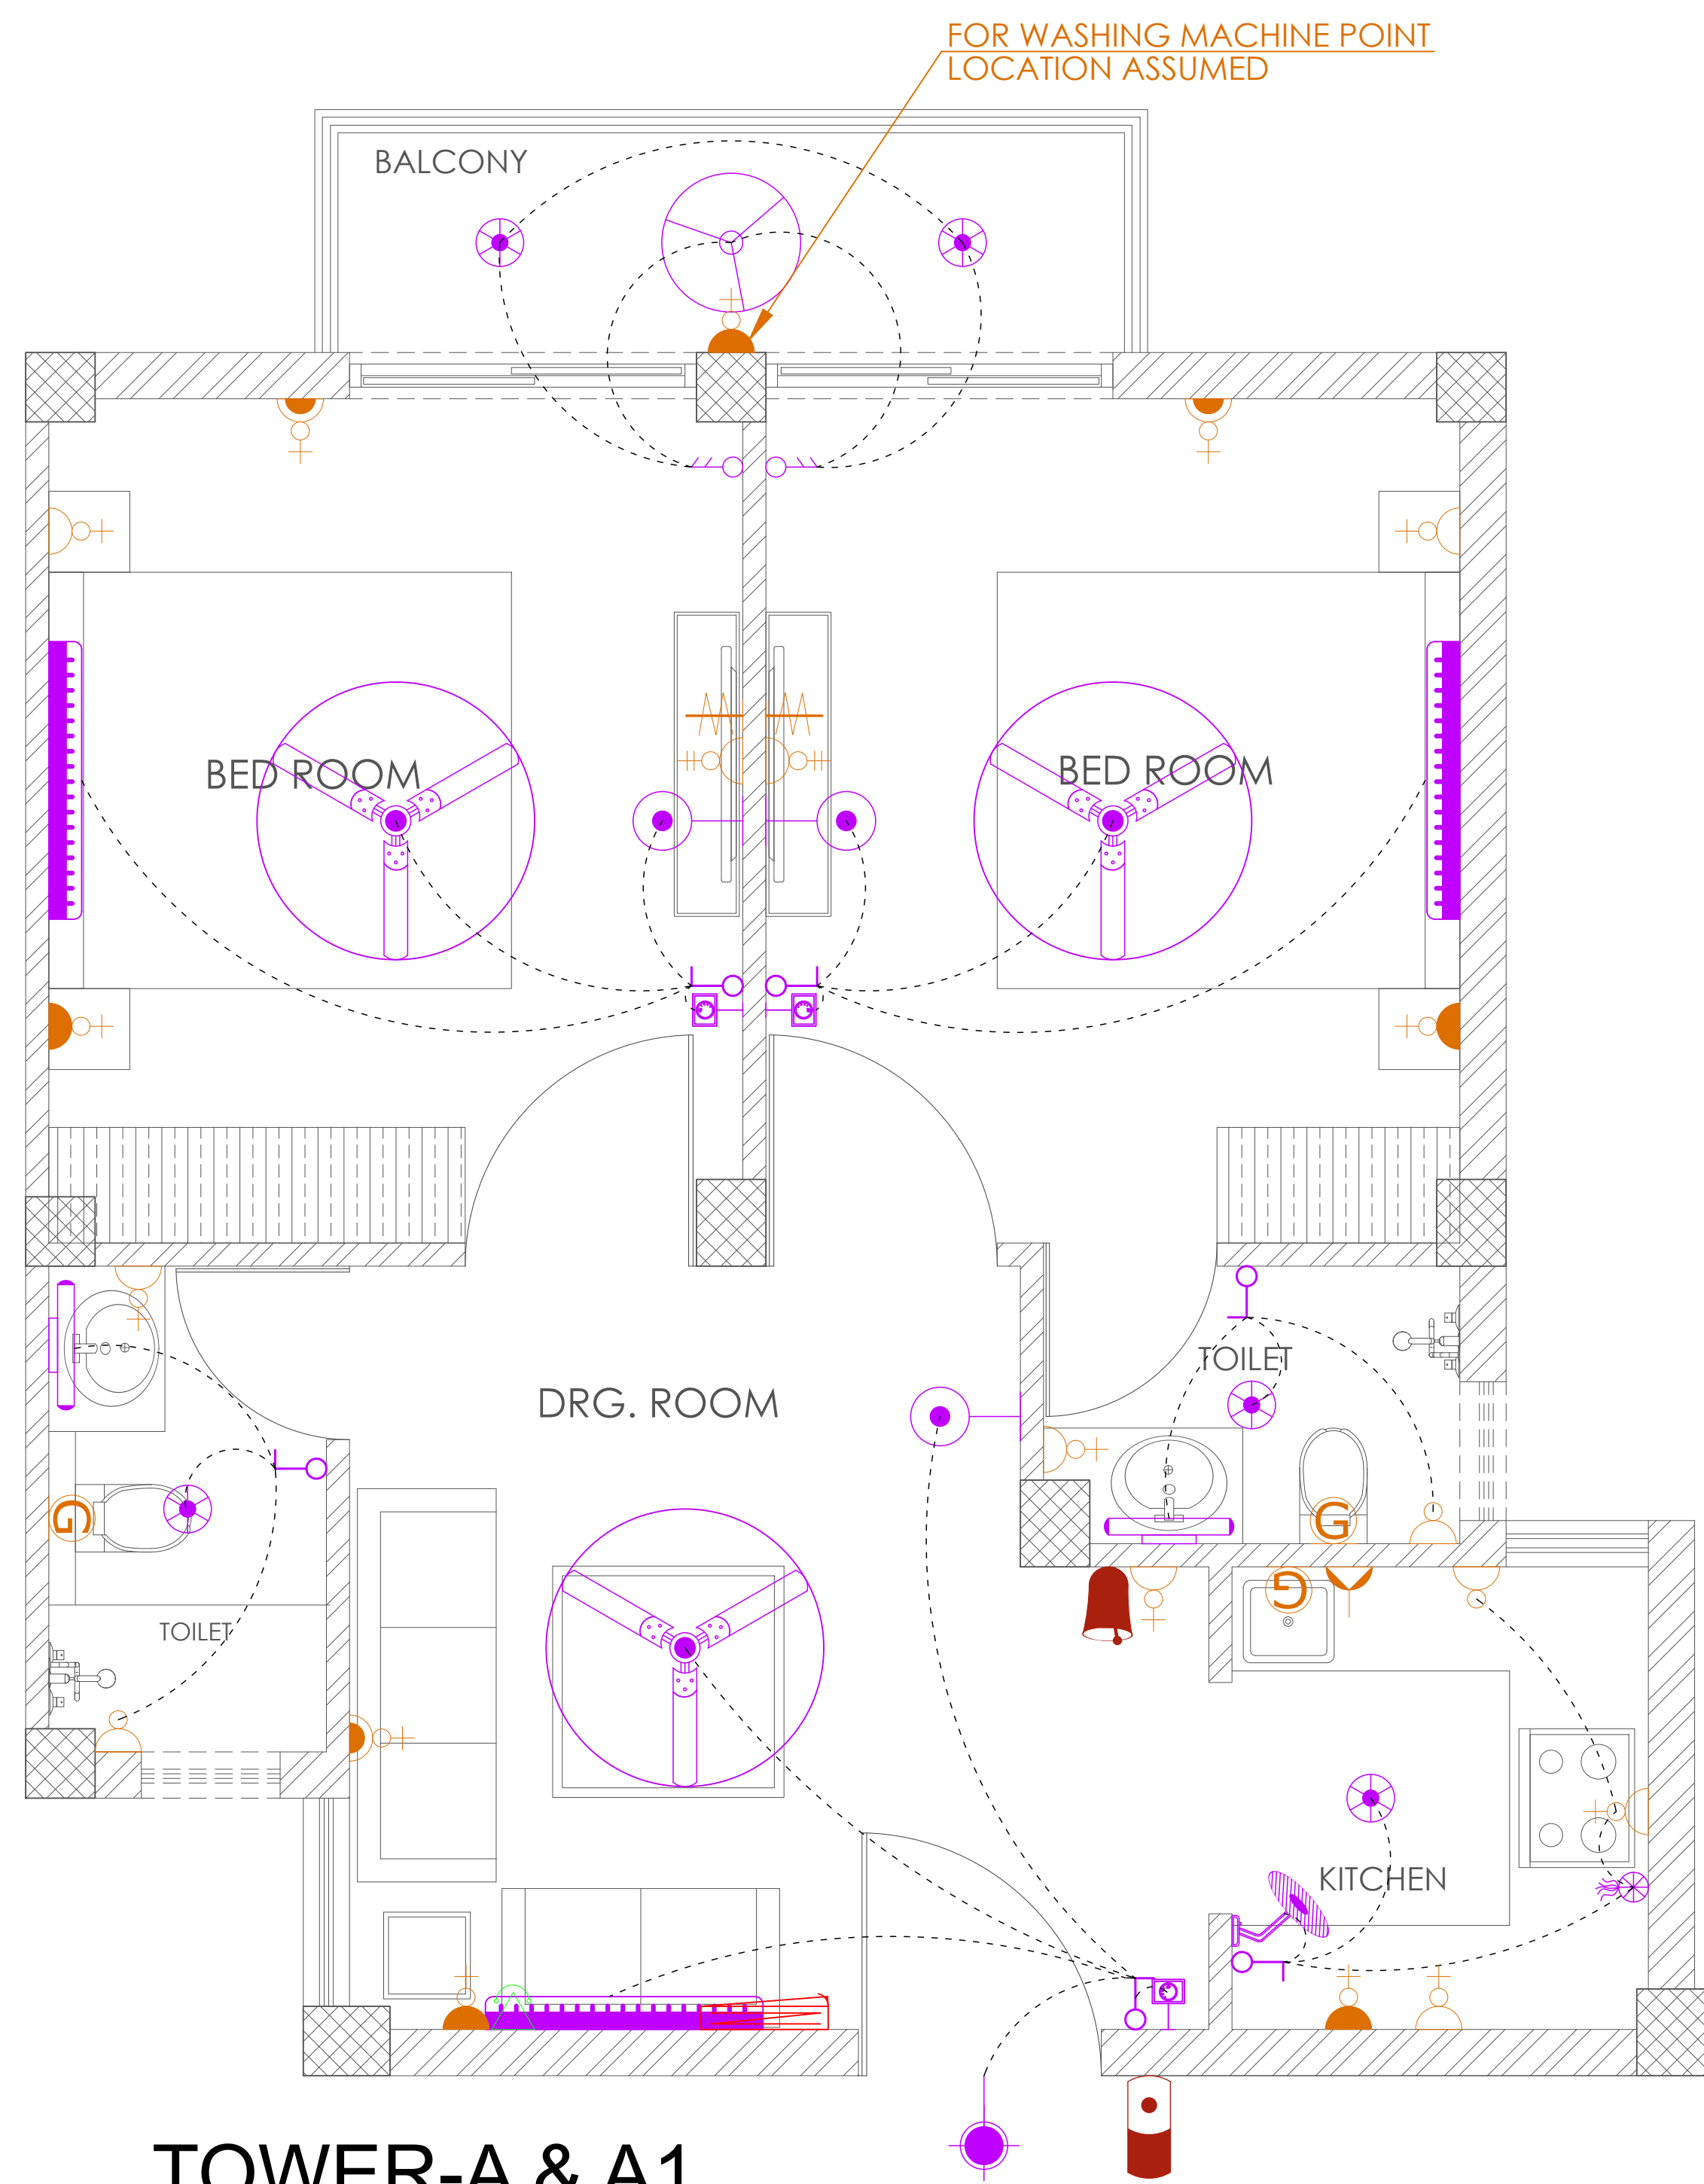

TOWER-A & A1
(FLOOR LAYOUT, UNIT WORKING PLAN)

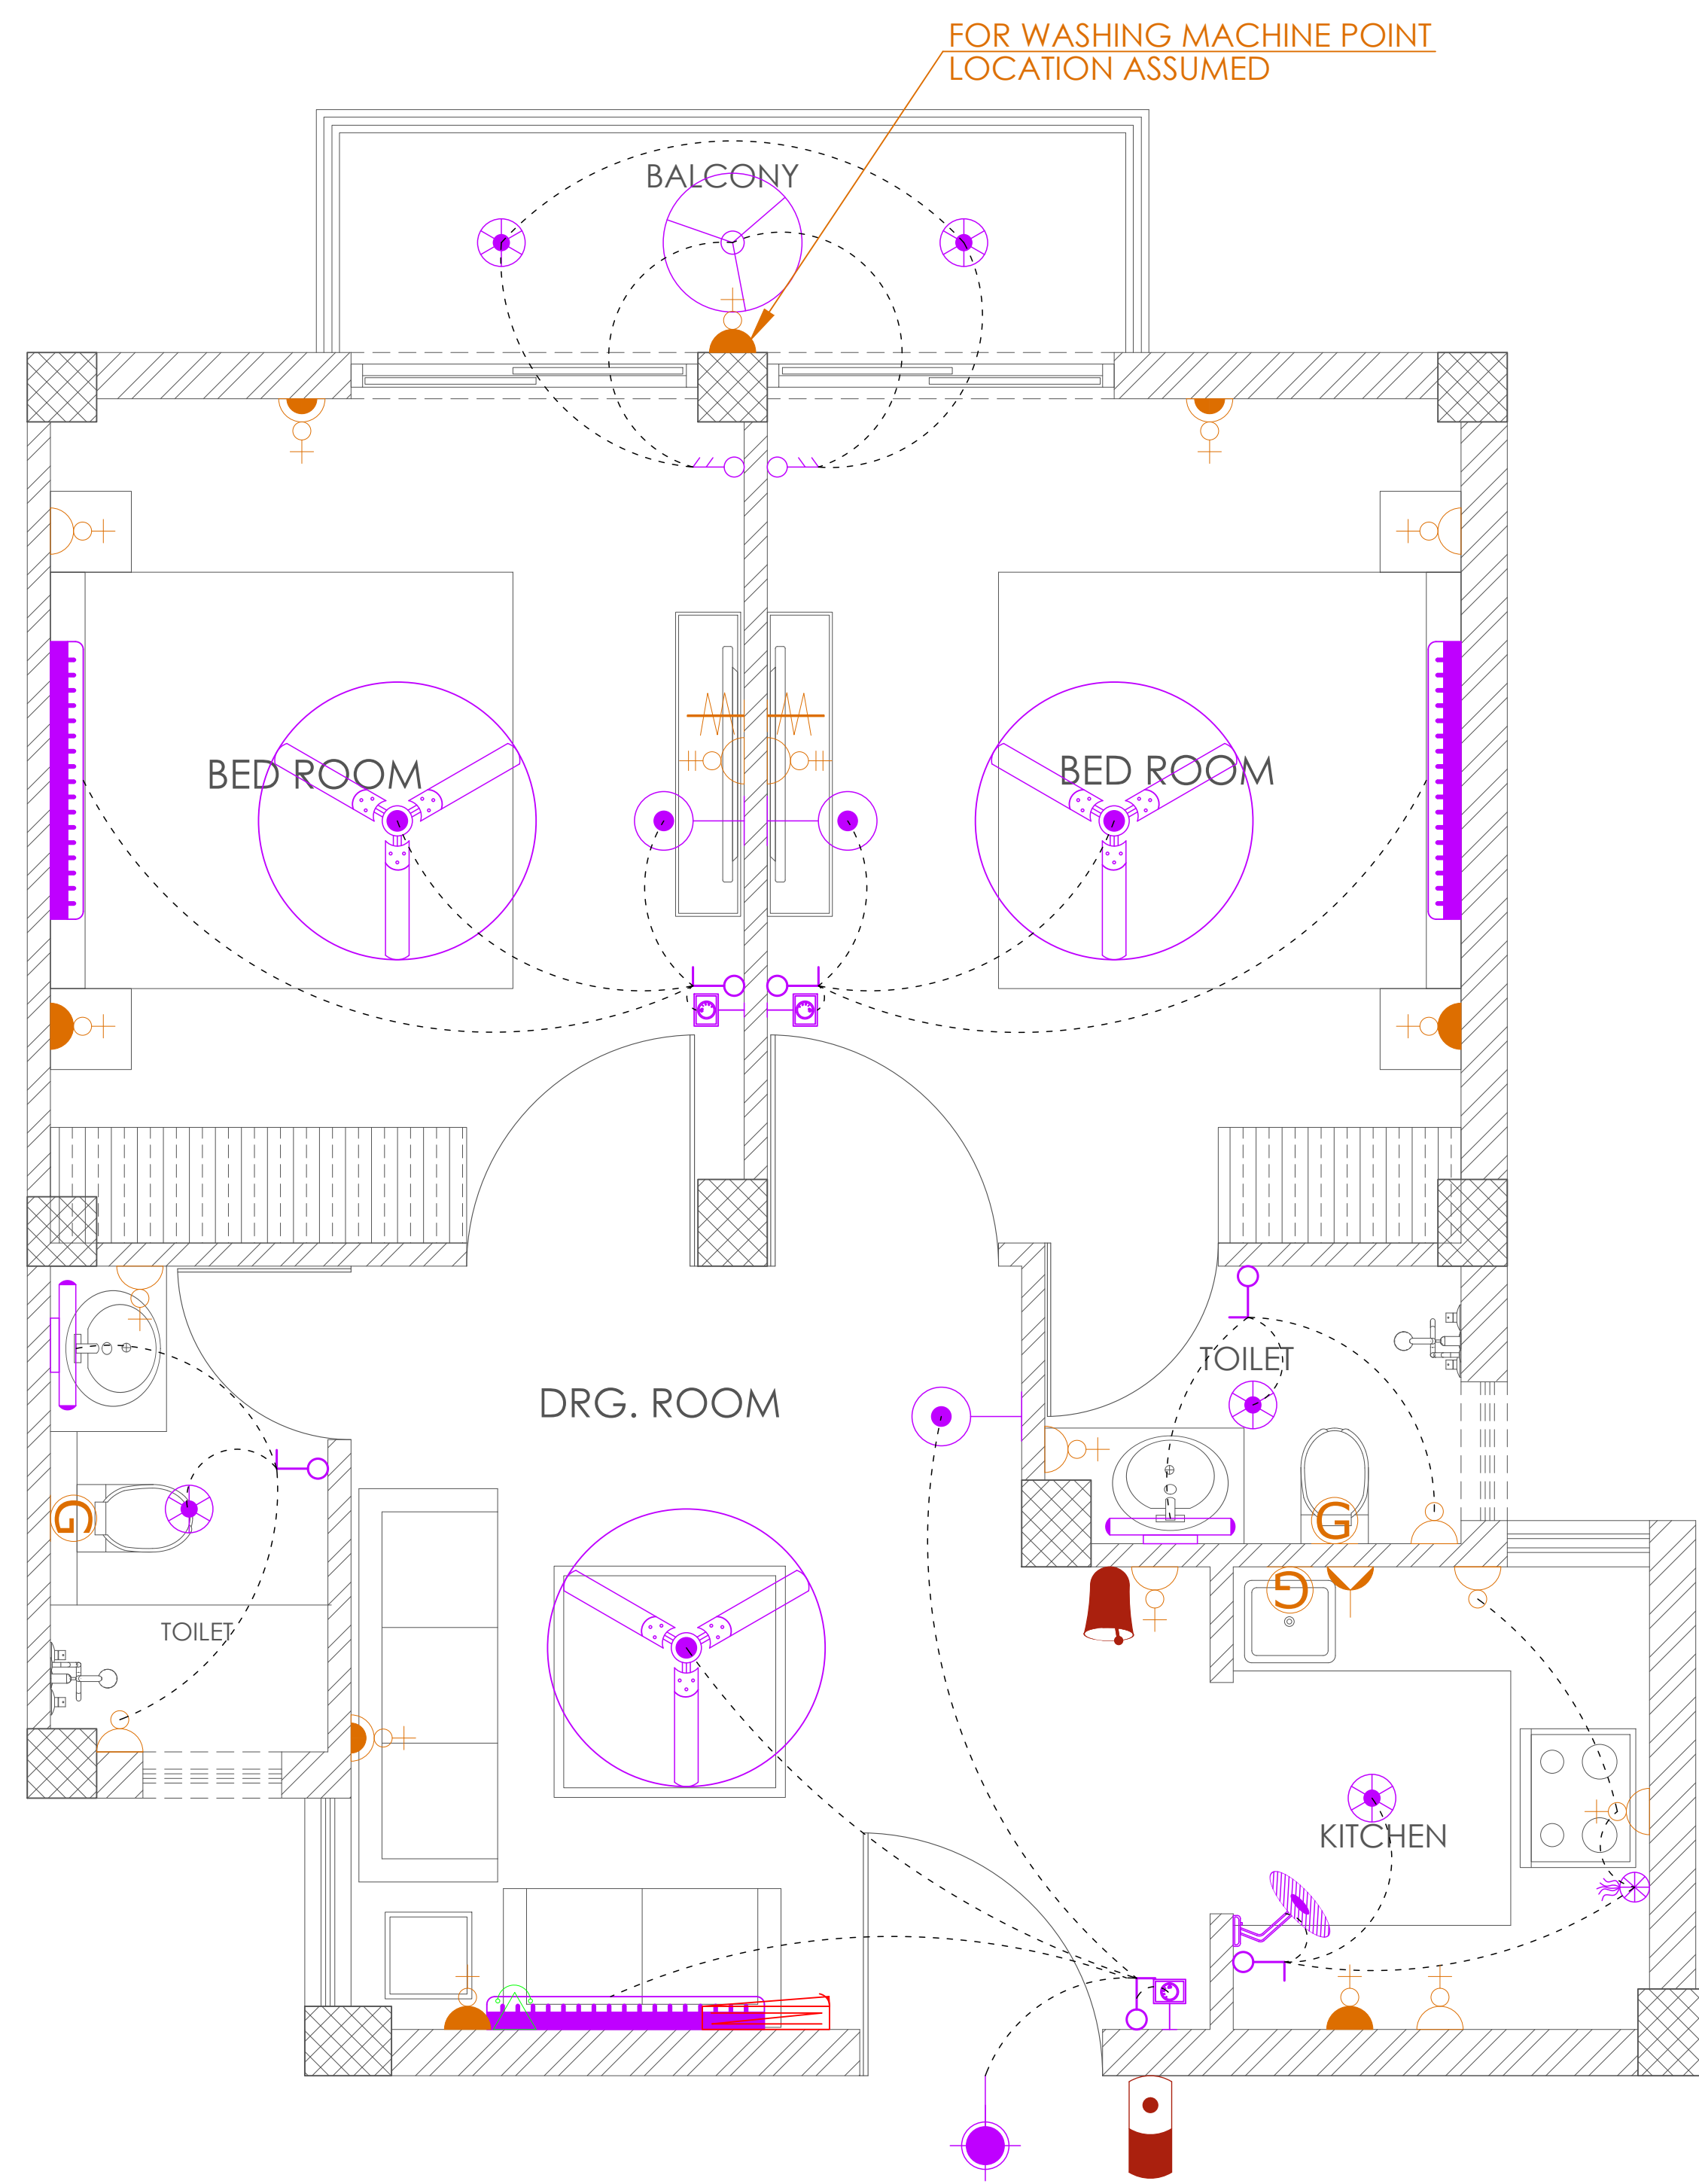

TYPICAL 2-BHK UNIT WORKING PLAN
(FLOOR LAYOUT, UNIT WORKING PLAN)

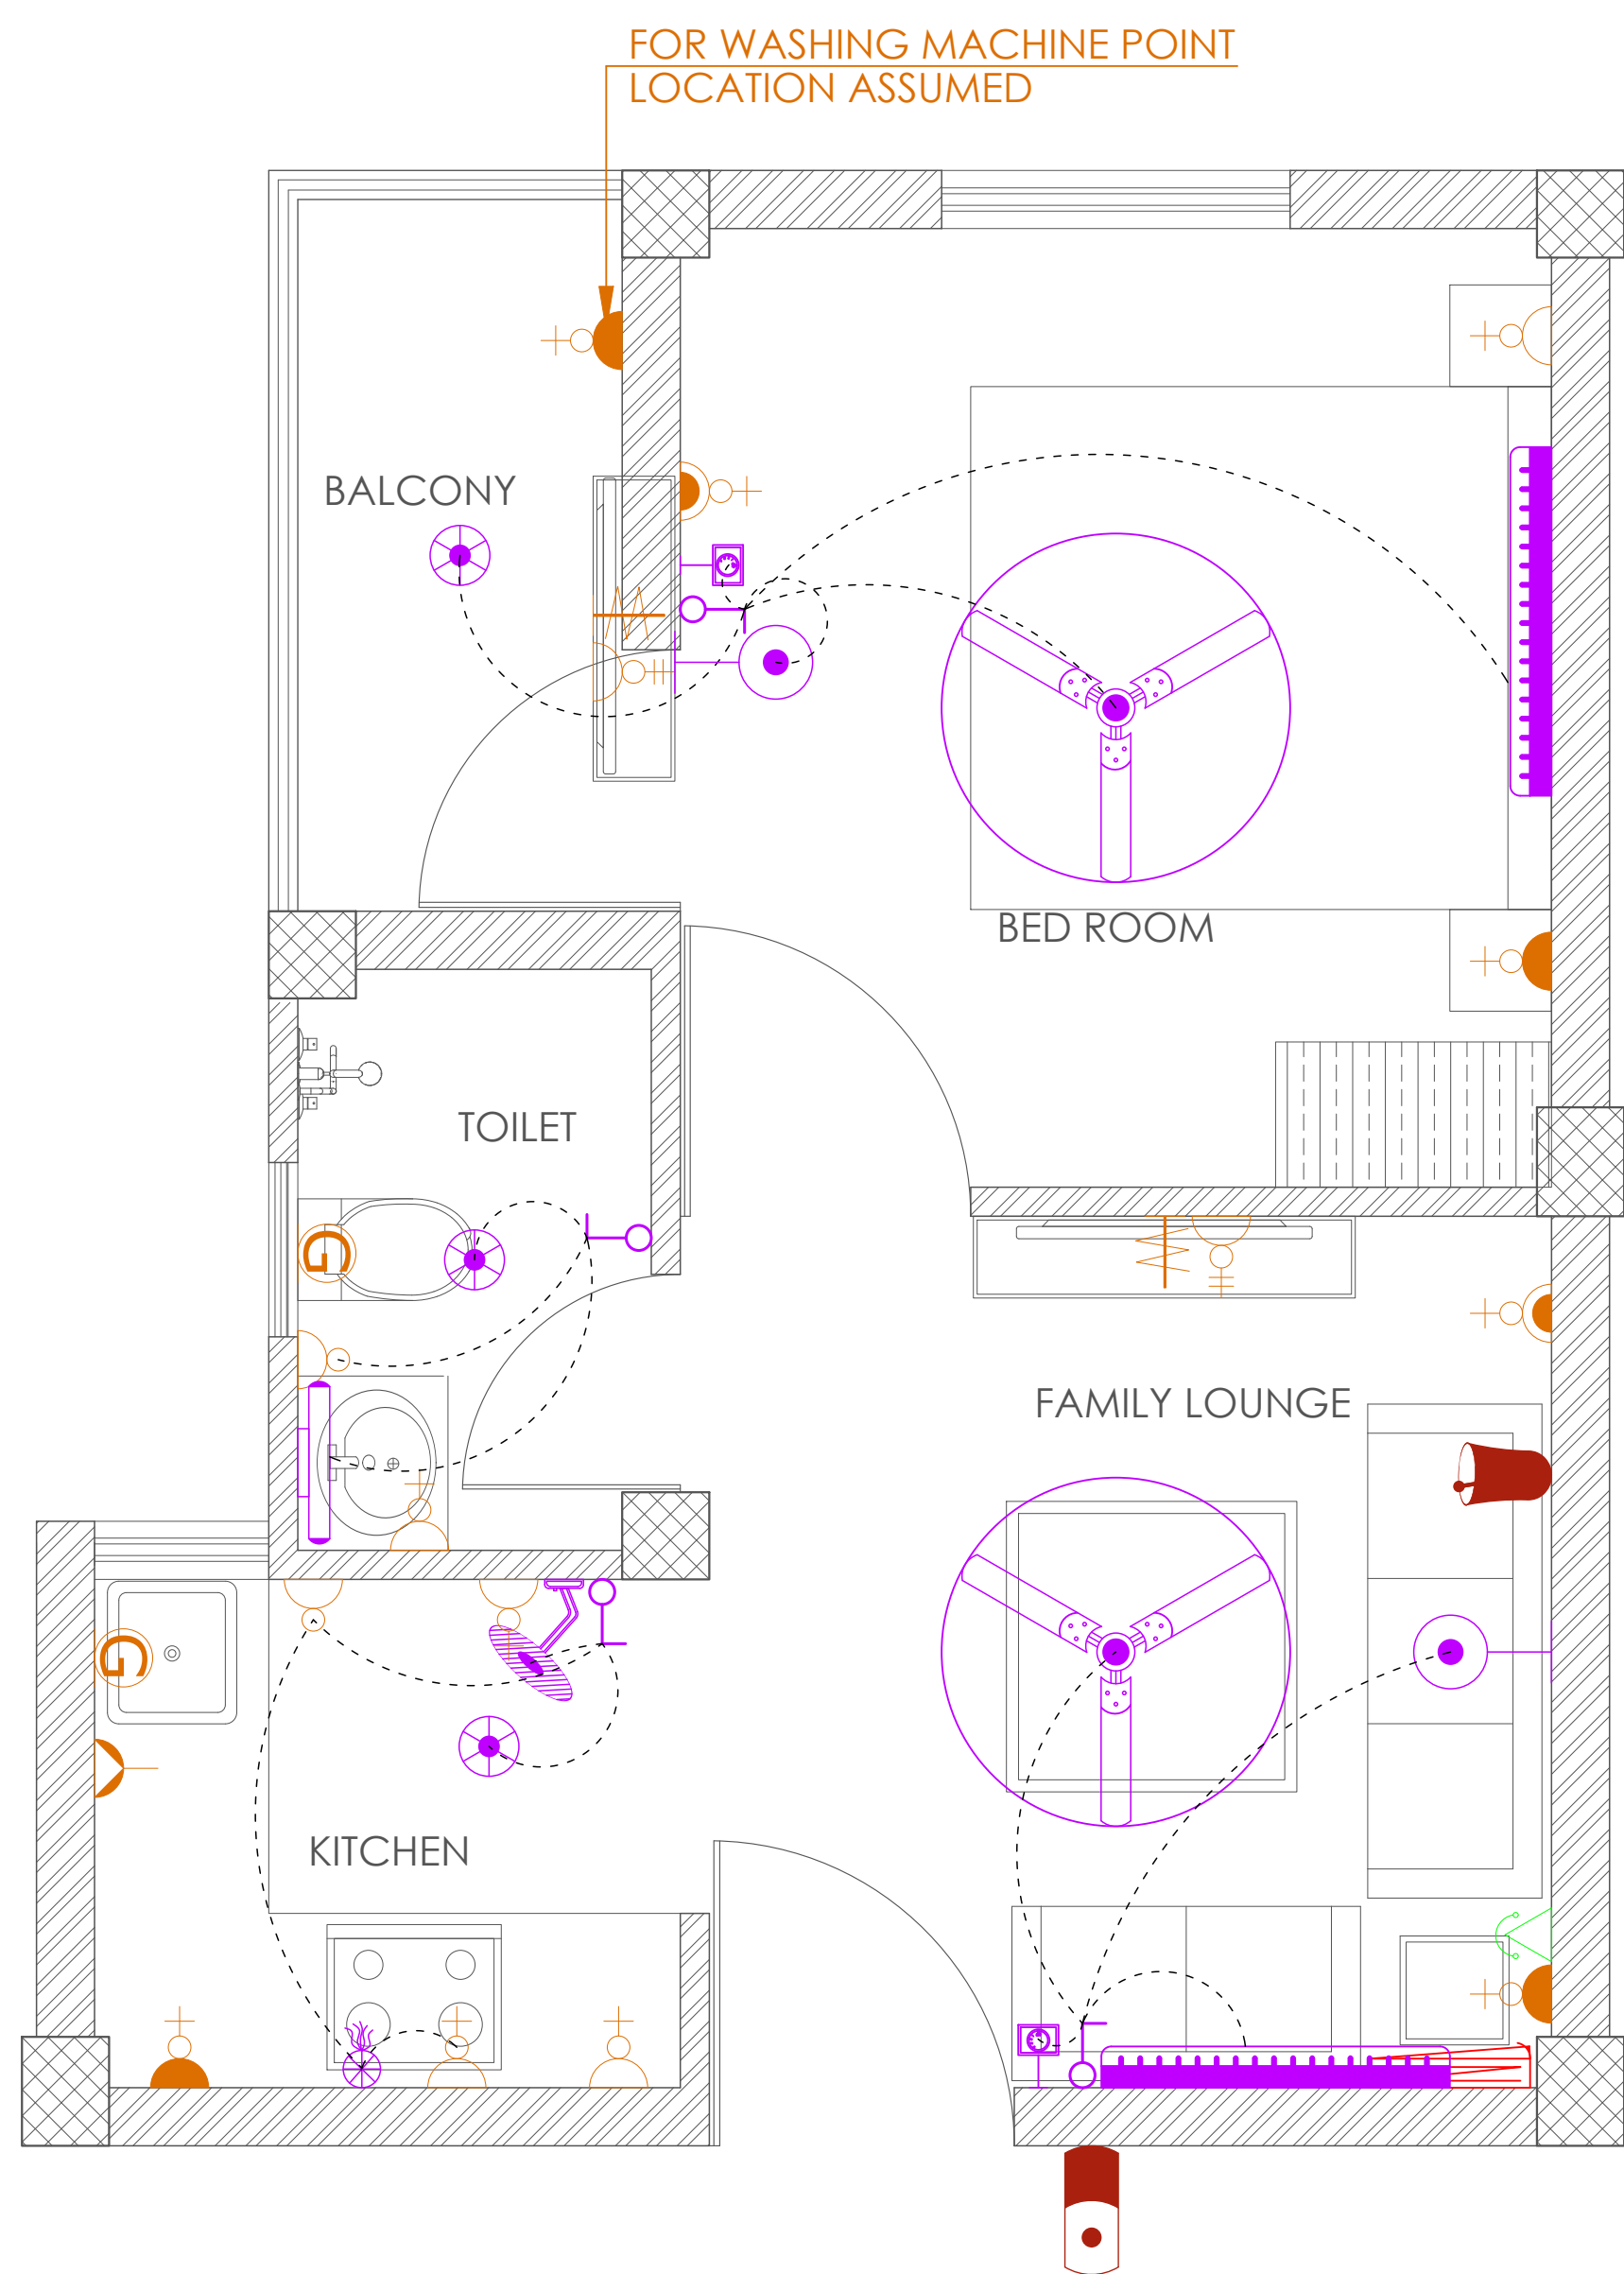

TYPICAL 1-BHK UNIT WORKING PLAN
(FLOOR LAYOUT, UNIT WORKING PLAN)

S.NO.	LEGENDS TABLE RAW POWER POINTs	
01.		1x6A ROUND SOCKET & 6A SWITCH
02.		2x6A ROUND SOCKET & 6A SWITCH
03.		1x6A ROUND SOCKET
04.		1x6/16A SOCKET & 16A SWITCH
05.		1x25A SOCKET & 25A SWITCH/MCB
06.		1x6/16A SOCKET NEAR GEYSER & 16A SWITCH
07.		TELEVISION OUTLET
08.		6A SOCKET & 6A SWITCH NEAR RO
09.		TELEPHONE / INTERCOM POINT
10.		DOUBLE DOOR DISTRIBUTION BOARD
S.NO.	LEGENDS TABLE LIGHTS	
01.		SURFACE MOUNT LED CEILING LIGHT
02.		18W LED BATTEN WALL LIGHT 1200MM
03.		BRACKET LIGHT
04.		DOOR LIGHT
05.		MIRROR LIGHT
06.		450 MM DIA WALL BRACKET FAN
07.		1200 MM DIA CEILING FAN
08.		600 MM DIA CEILING FAN
09.		LOOSE WIRE POINT SIZE AS PER LOAD
10.		SWITCH BOARD
11.		2WAY SWITCH AT BED SIDE
12.		FAN REGULATOR
13.		ELECTRICAL LIGHTING LOOPING
14.		DOOR BELL SWITCH
15.		BUZZER

REVISION NUMBERS		
REV. NO	DATE	DESCRIPTION
RO	25.10.23	ISSUED FOR APPROVAL
CLIENT		
M/S GENNXT INFRA TECH PVT. LTD.		
PROJECT NAME		
PROPOSE HOUSING UNDER CM JAN AWAS YOJNA M/S GENNXT INFRA TECH PVT. LTD. AT KHASRA NO. 212,213, VILLAGE - NEEMRANA,TEH. NEEMRANA,DIST.ALWAR (RAJ.)		
ARCHITECT		
Shilpkar Architects Pvt. Ltd. Sustainable Green Architecture architects, engineers, valuers, project managers OFF. - 909, 9th Fl., ILD Trade Centre, Sec.-47, Sohna Road, Gurgaon. Ph. No. - 0124-4361909 OFF. - Hotel Regency Complex Bhiwadi (Rajasthan) Ph. No. - 01493-221766 OFF. - 307, 308, Central Plaza, CC2, EPIP, Neemrana (Rajasthan) e-mail - info@sapind.in, info@gn@sapind.in, info@n@sapind.in		
ELECTRICAL SERVICES CONSULTANT		
ECMS INDIA PVT. LTD. WP-21 C-282, BASEMENT NOIDA SECTOR-71, UTTAR PRADESH-201307 E-mail:- ecms.tech01@gmail.com URL:- www.ecmsindia.com Ph.No. 0120-3502815		
DRAWING TITLE- EL-LIGHTING & POWER LAYOUT TOWER-A, A1 & TOWER-B & B1		
☒ FOR APPROVAL		☐ ADVANCE COPY
☐ TENDER DRAWING		☐ GOOD FOR CONSTRUCTION
DRAWN BY	SHADAB	REV NO. RO(25.10.2023)
CKD BY	SANJAY	SCALE N.T.S.
FIN. YEAR	2023-24	JOB NO. 2476
DRAWING NO.		GENNXT/ECMS/TYP/EL-01